

Search:

Beaver Tails Milton - Fit Out [34 Pages]

2021-08-30 2103118 Re-issued for BP Tender (1) (1)

2021-08-30 2103118 Re-issued for BP Tender (1) (1)

2021-08-30 2103118 Re-issued for BP...

New Count 2.0 EA

1 1540.9 sq ft

2021-08-30 2103118 Re-issued for BP Tender (1) (1)

2021-08-30 2103118_Re-issu...

2021-08-30 2103118_Re-issued for BP_Tender (1) (1)

2021-08-30 2103118 Re-issued for BP ...

2021-08-30 2103118_Re-issued for BP_Tender (1) (1)

2021-03-30 2103118_Re-issued for BP_...

2021-08-30 2103118_Re-issued for BP_Tender (1) (1)


2021-08-30 2103118 Re-issued for BP_Tender (1) (1)

2021-08-30 2103118 Re-issued for BP Tender (1) (1)

2021-08-30 2103118_Re-issued for BP_Tender (1) (1)

2021-08-30 2103118_Re-issued for BP_Tender (1) (1)

[illegible][illegible]

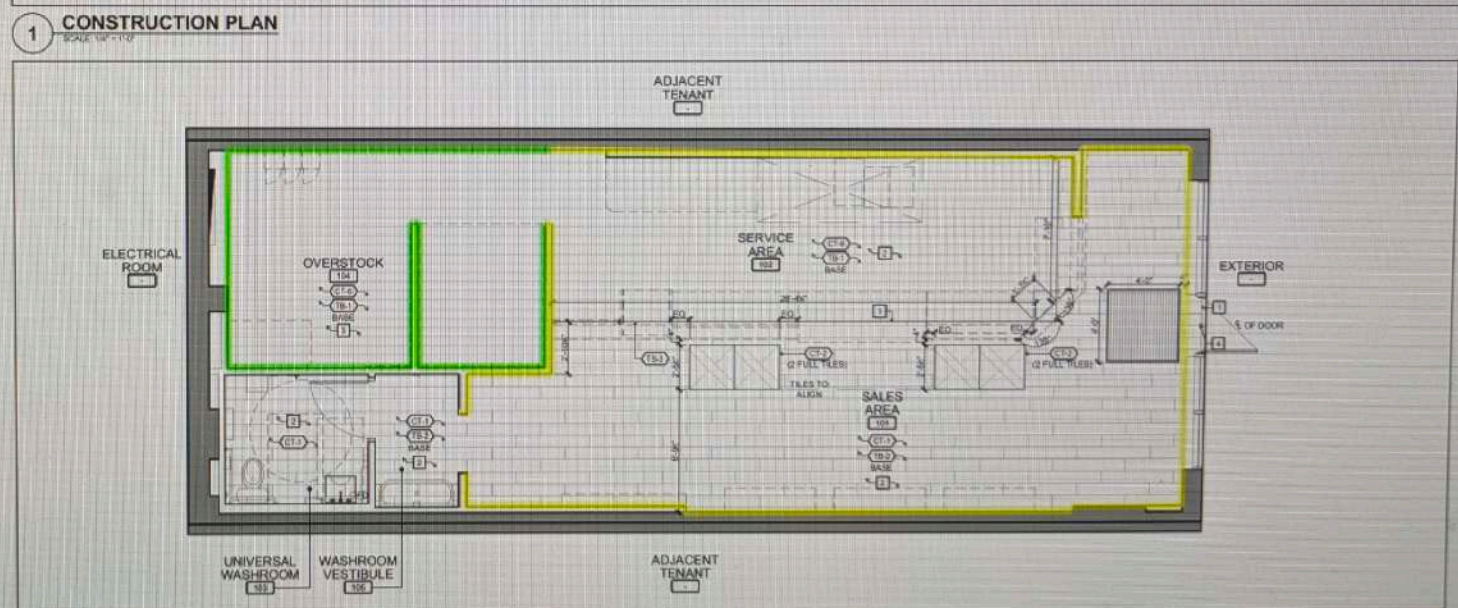

7. EXTENDING STOREFRONT FRAME AND GLAZING. CLEAN TO LIKE NEW CONDITION.
8. EXTENDING STOREFRONT ENTRY DOOR (W/ NEW FRESH - REFER TO DOOR SCHEDULE FOR DETAILS.
9. LOCATION OF EXISTING ELECTRICAL PANEL.
10. B.C. TO INSTALL NEW WASHROOM PLUMBING FIXTURES. REFER TO MECHANICAL DRAWINGS FOR SPECIFICATIONS.
11. CEILING IS PLUMB RECEIVED ENTRANCE HAT BY CORRESPONDING CANADA COUNTRY BLACK GR. CHEMICAL CARRYER ASSETS, SUPPLIED AND INSTALLED BY B.C.
12. SLOPED LINE INDICATES EXTENT OF FULL HEIGHT FRP PANEL (SEE) APPL. SLOPED LINE TO ALL EDGES.
13. SLOPED LINE INDICATES PROPOSED FIXTURES, MILLWORK AND EQUIPMENT.
14. SHOW EXIST. OR NEW CONSTRUCTION TO BE IN LINE WITH EXIST. FACE.

- 1 G.C. TO ENSURE A SMOOTH TRANSITION BETWEEN FINISHES.
2 REFER TO ELEVATIONS FOR WALL FINISHES.
3 ALL ENTRY/ROOM WALLS TO RECEIVE PAINT PRIMER (C-1)
4 STARTING POINT OF (C-5)